
Сушильный Палет для 5 дневной сушки кирпича

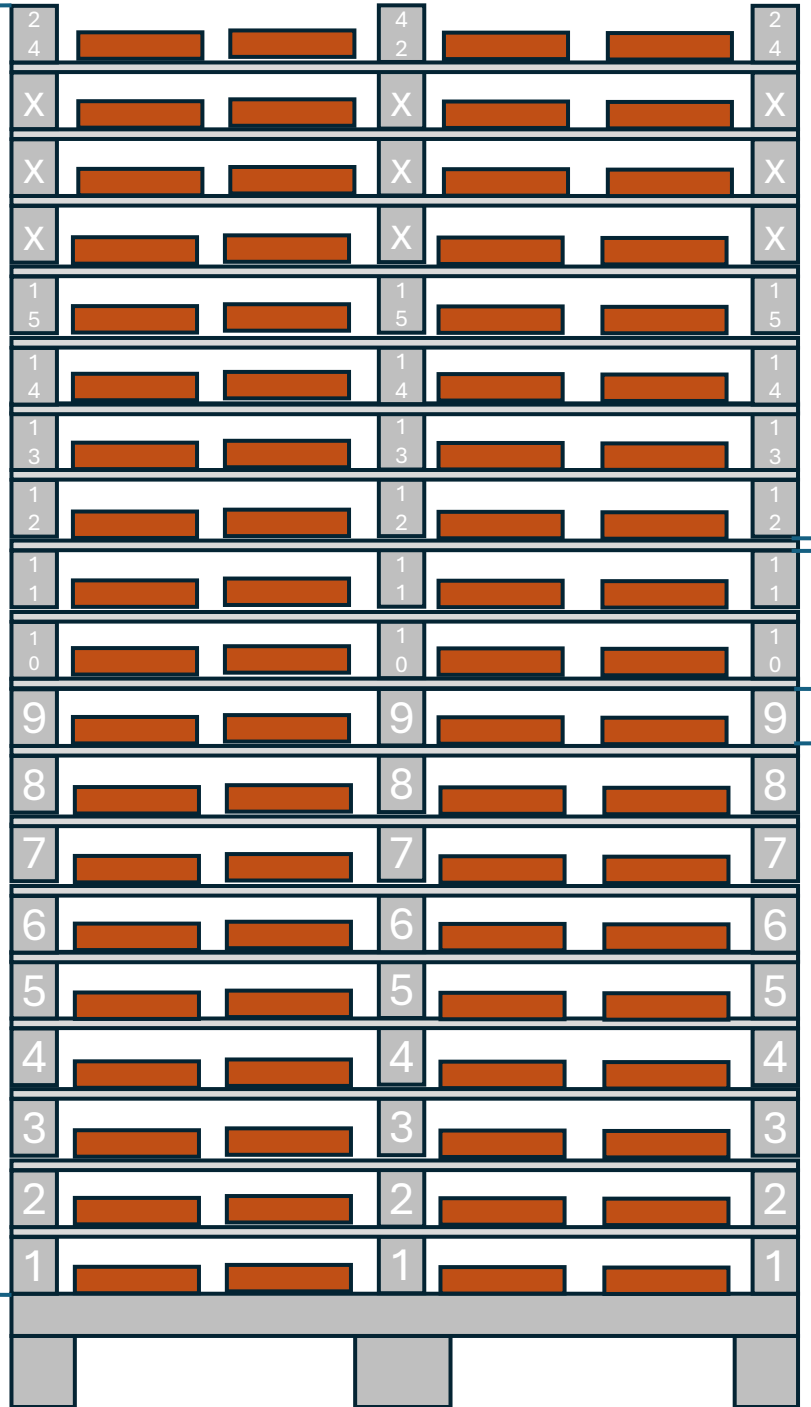


Высота плиты 8 мм или 10 мм Интегрируема в перемитральные подставки

Размер перемитральных кубов 3х3х7

Состоит из 24 уравней общей высотой 1 метр 68 см. Общее колличесво кирпича на этаж 16 Всего к сушке 384 кирпича

Сушильный Палет для 5 дневной сушки кирпича Уравень

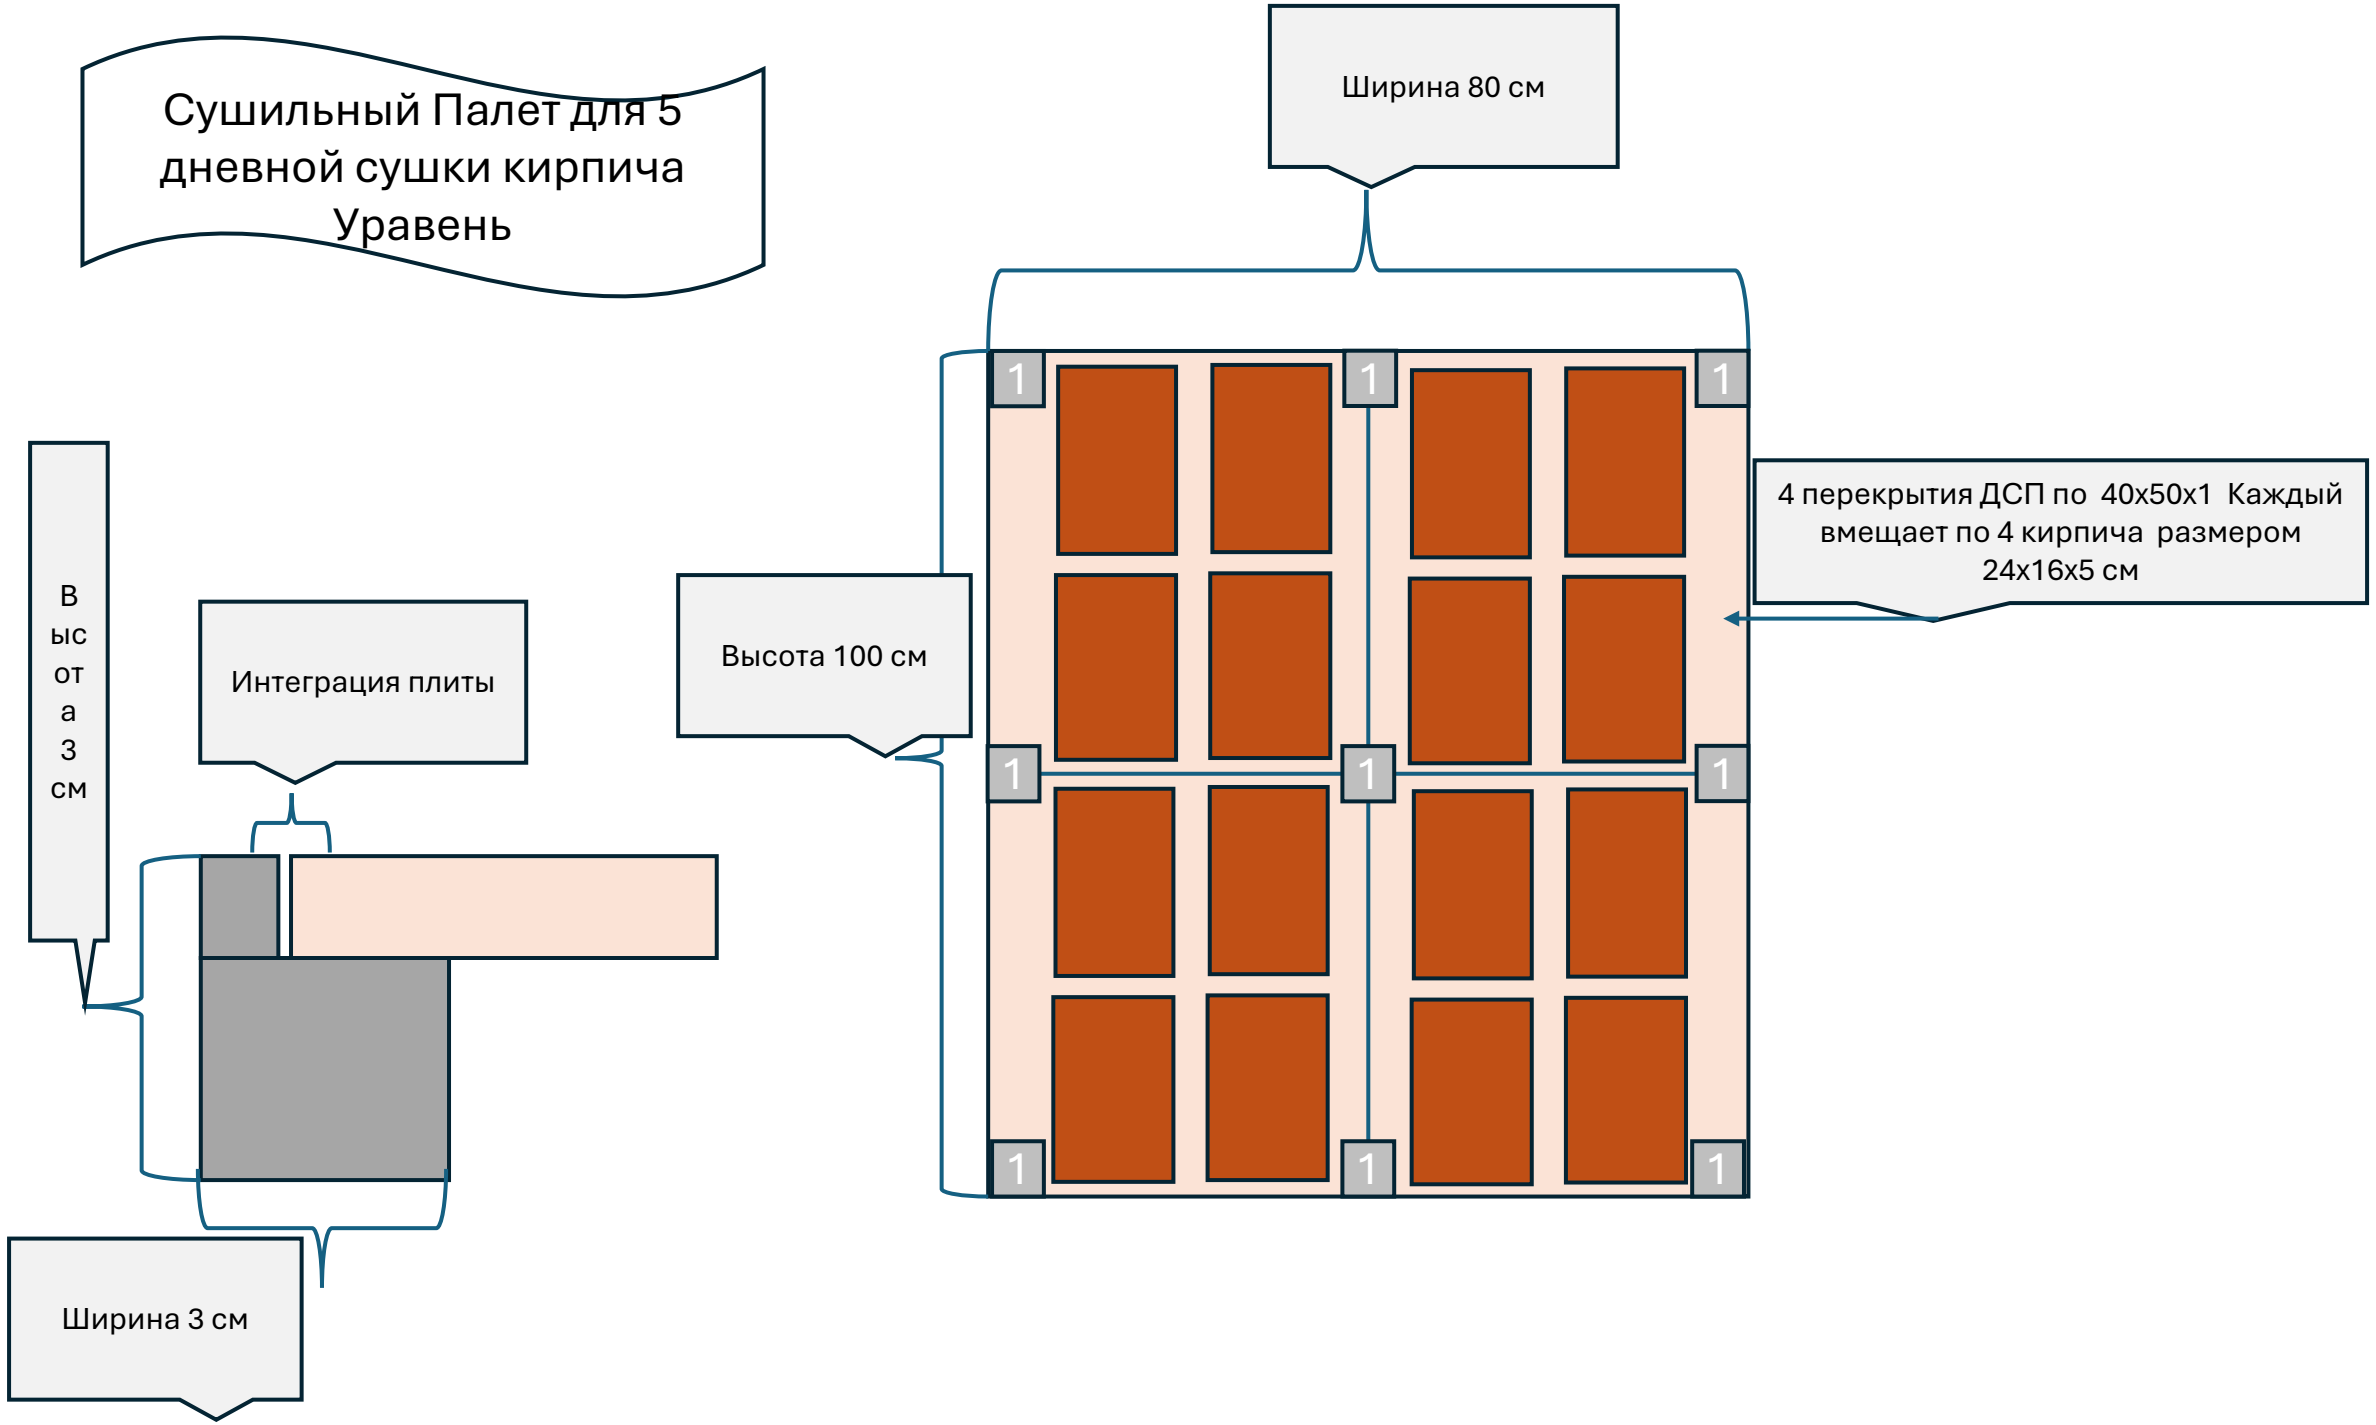

Рабочая зона


Длинна 100 м

5 дневный этап сушки кирпича 8 Стендов

25 дневный этап сушки кирпича





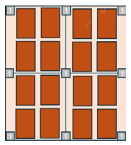













Суточьный тонаж Глины для кирпича в 2 КГ 6856 Килограм



2 этажный транспалет